


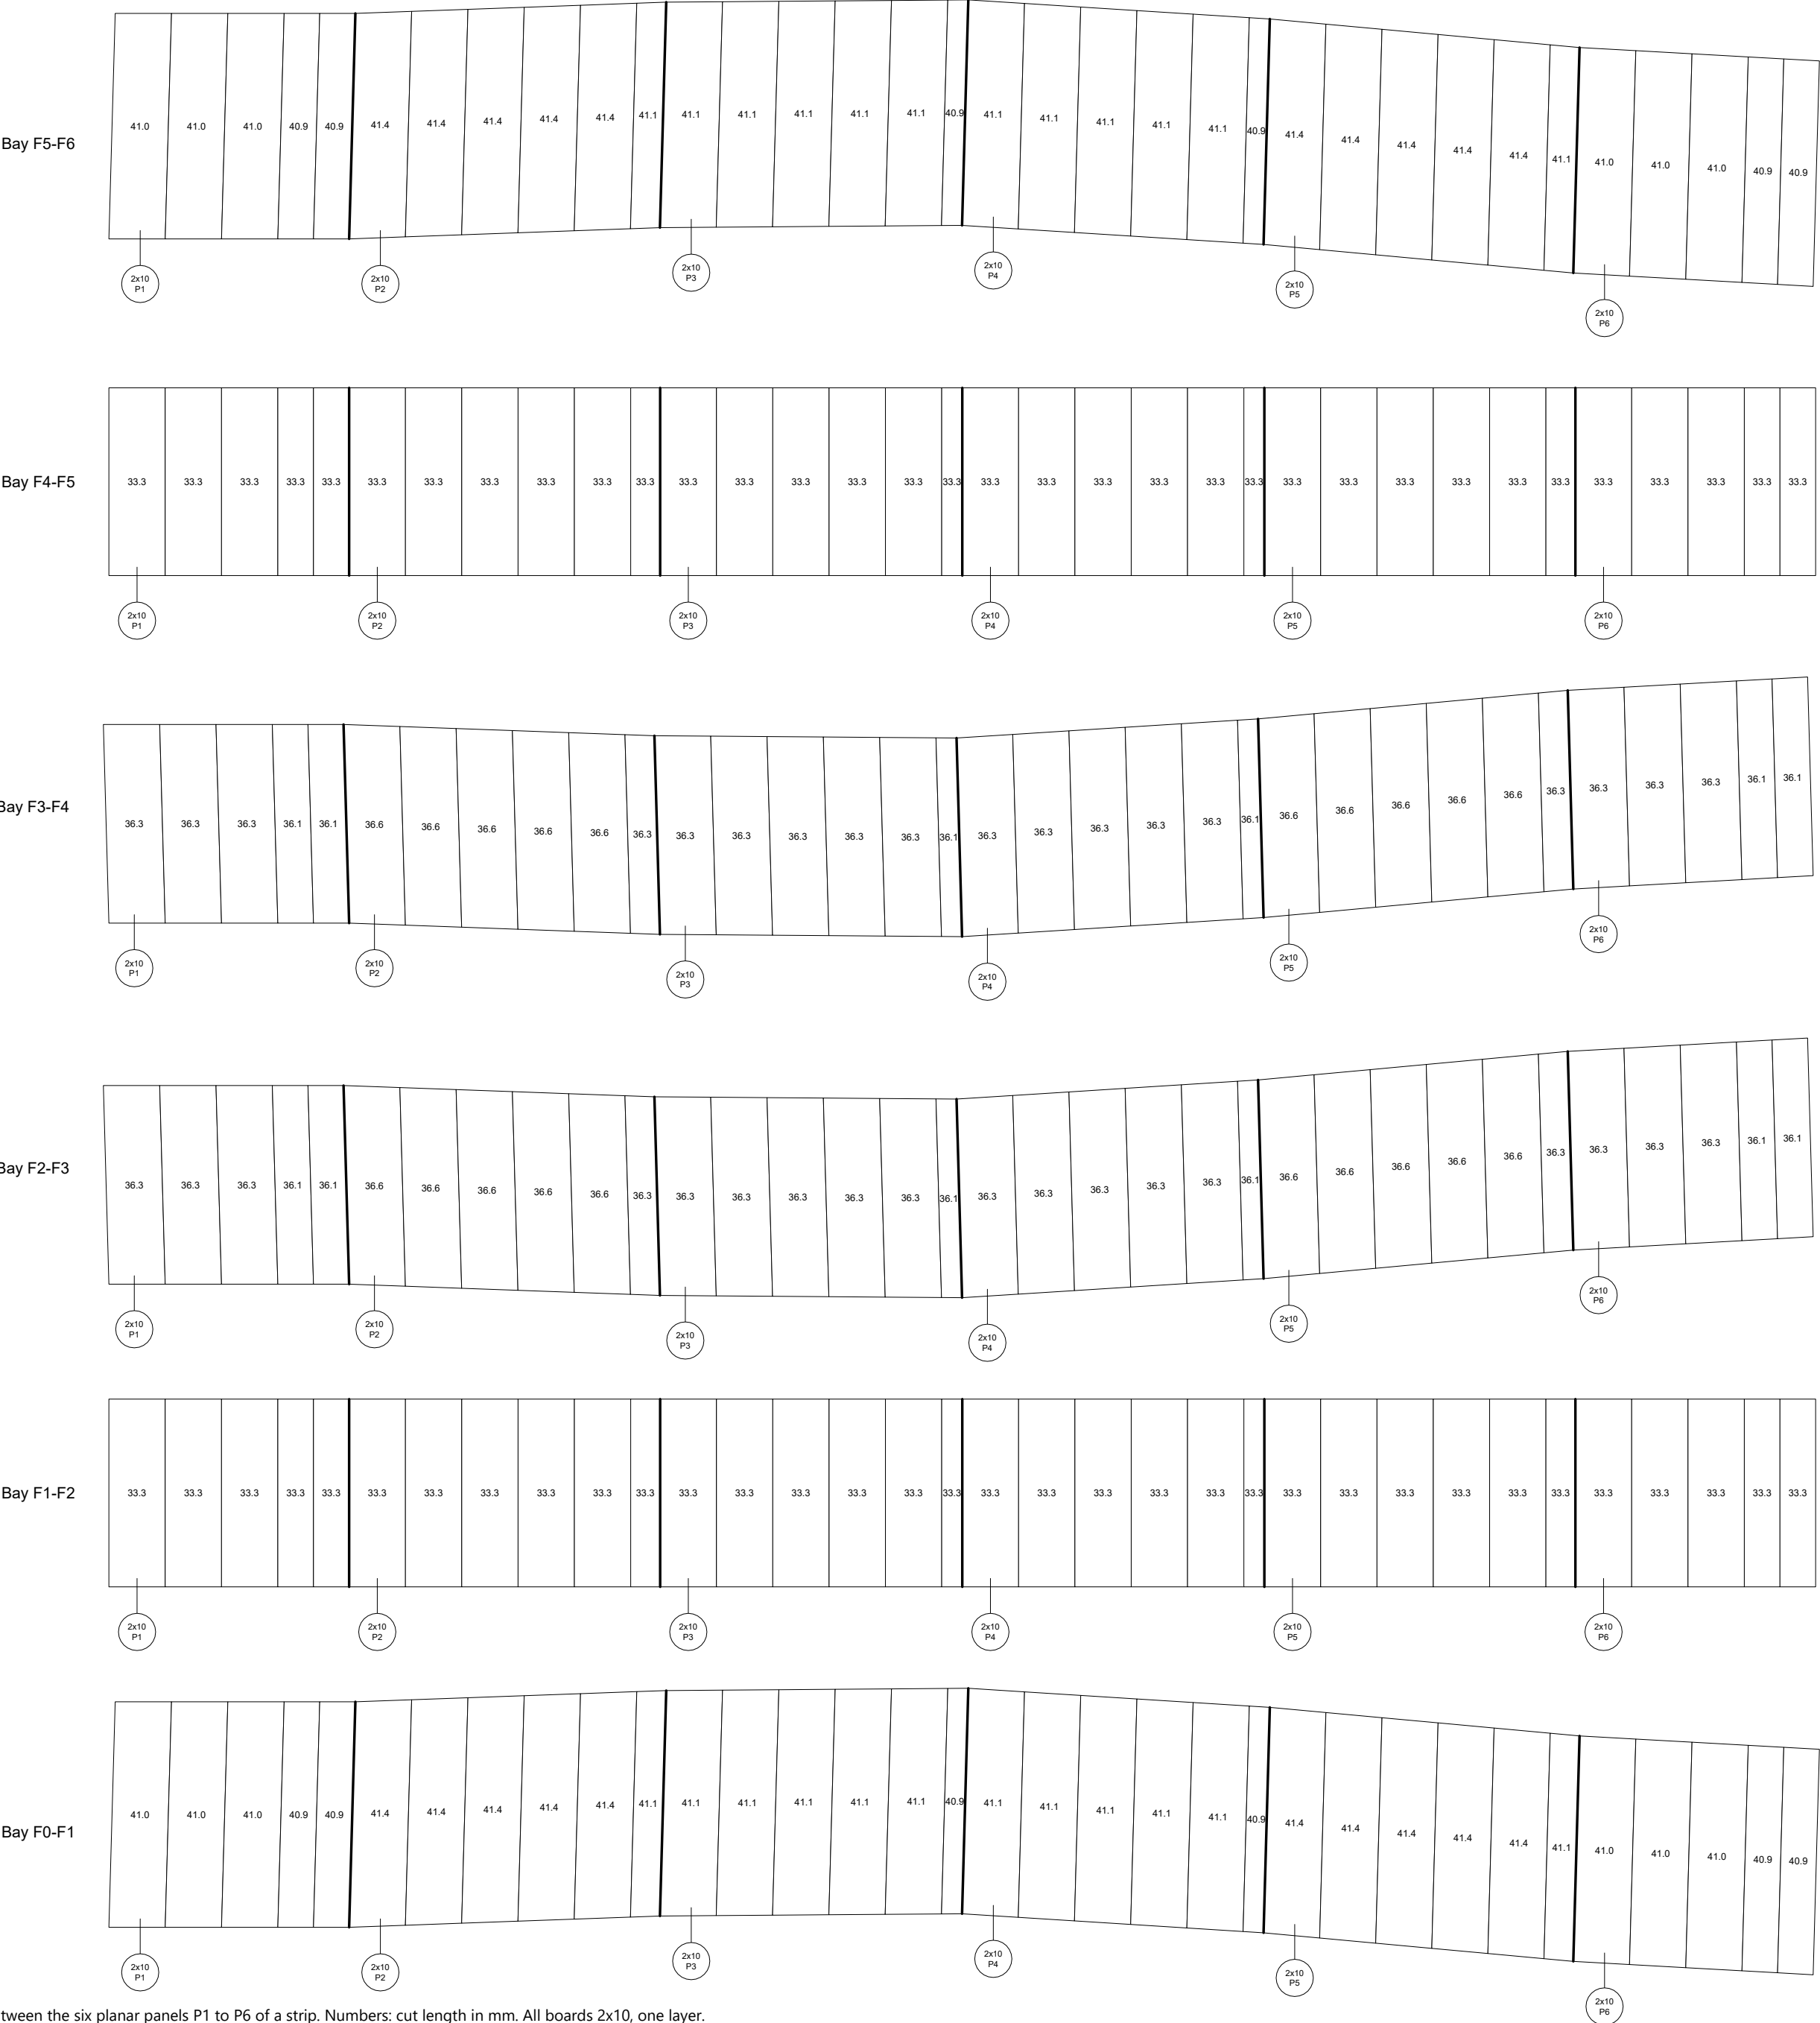

NOTE Roof boards of each bay laid flat, door end at the bottom, -x on the left. Heavy lines: folds between the six planar panels P1 to P6 of a strip. Numbers: cut length in mm. All boards 2x10, one layer.

